

7
DIBUJITOS A CORTAR

11
PAÑOS DE PIQUES

85
PIQUES DE 38"

19
POSTES DE 48"

6
SECCIONES SOLDADAS

OJO — esta hoja es **SOLO** de la **caballeriza 2**, el **cuarto balcón**. Las letras N, P, Q y R no se repiten en ninguna otra hoja. **Falta confirmar el orden en que se encadenan las corridas** alrededor del edificio: los largos y el despiece no cambian, solo cuál sección lleva cada poste de esquina. El pañito del signo de interrogación no está en esta hoja: falta medirlo.

REPARTO DE LAS CORRIDAS

Balcón	Corrida	Largo total	Secciones soldadas
Caballeriza 2	Corrida N	441-3/8" (36'-9-3/8")	N-1 + N-2 + N-3
Caballeriza 2	Corrida P	191-3/8" (15'-11-3/8")	P-1
Caballeriza 2	Corrida Q	99" (8'-3")	Q-1
Caballeriza 2	Corrida R	48" (4'-0")	R-1


CORTE DE LOS 7 DIBUJITOS — LISTA COMPLETA


Pieza	Sección	Largo de corte	Por dibujo	Total 7	Nota
V	1×1×1/16	38"	2	14	vertical del cuadro · corte recto
B	1×1×1/16	38"	2	14	pique de flanco · corte recto
H	1×1×1/16	28-1/4"	2	14	horizontal del cuadro · corte recto
D1	1×1×1/16	39-15/16"	1	7	diagonal entera · 45°/45° punta a punta
D2	1×1×1/16	19-7/16"	2	14	media diagonal · 45° un lado, recta el otro
C2	1×1×1/16	19-1/16"	4	28	rombo Q2 · 45°/45° · cara corta 17-1/16
C3	1×1×1/16	9-5/16"	4	28	rombo Q3 · 45°/45° · cara corta 7-5/16

Material 1×1×1/16 para los dibujitos: 234 pies lineales ≈ 13 tiras de 20' (sin contar desperdicio de corte ni los piques de los paños lisos).

Los largos C2 y C3 ya llevan descontado el material de la X. C2 = 19-1/16 punta larga / 17-1/16 cara corta. C3 = 9-5/16 punta larga / 7-5/16 cara corta. **No le quites despunte**: asientan a ras contra la diagonal.

SECCIÓN N-1 CABALLERIZA LADO 2 · 148-7/8" (12'-4-7/8") · 4 postes · 1 dibujo · 2 paños de piques (20 piques)

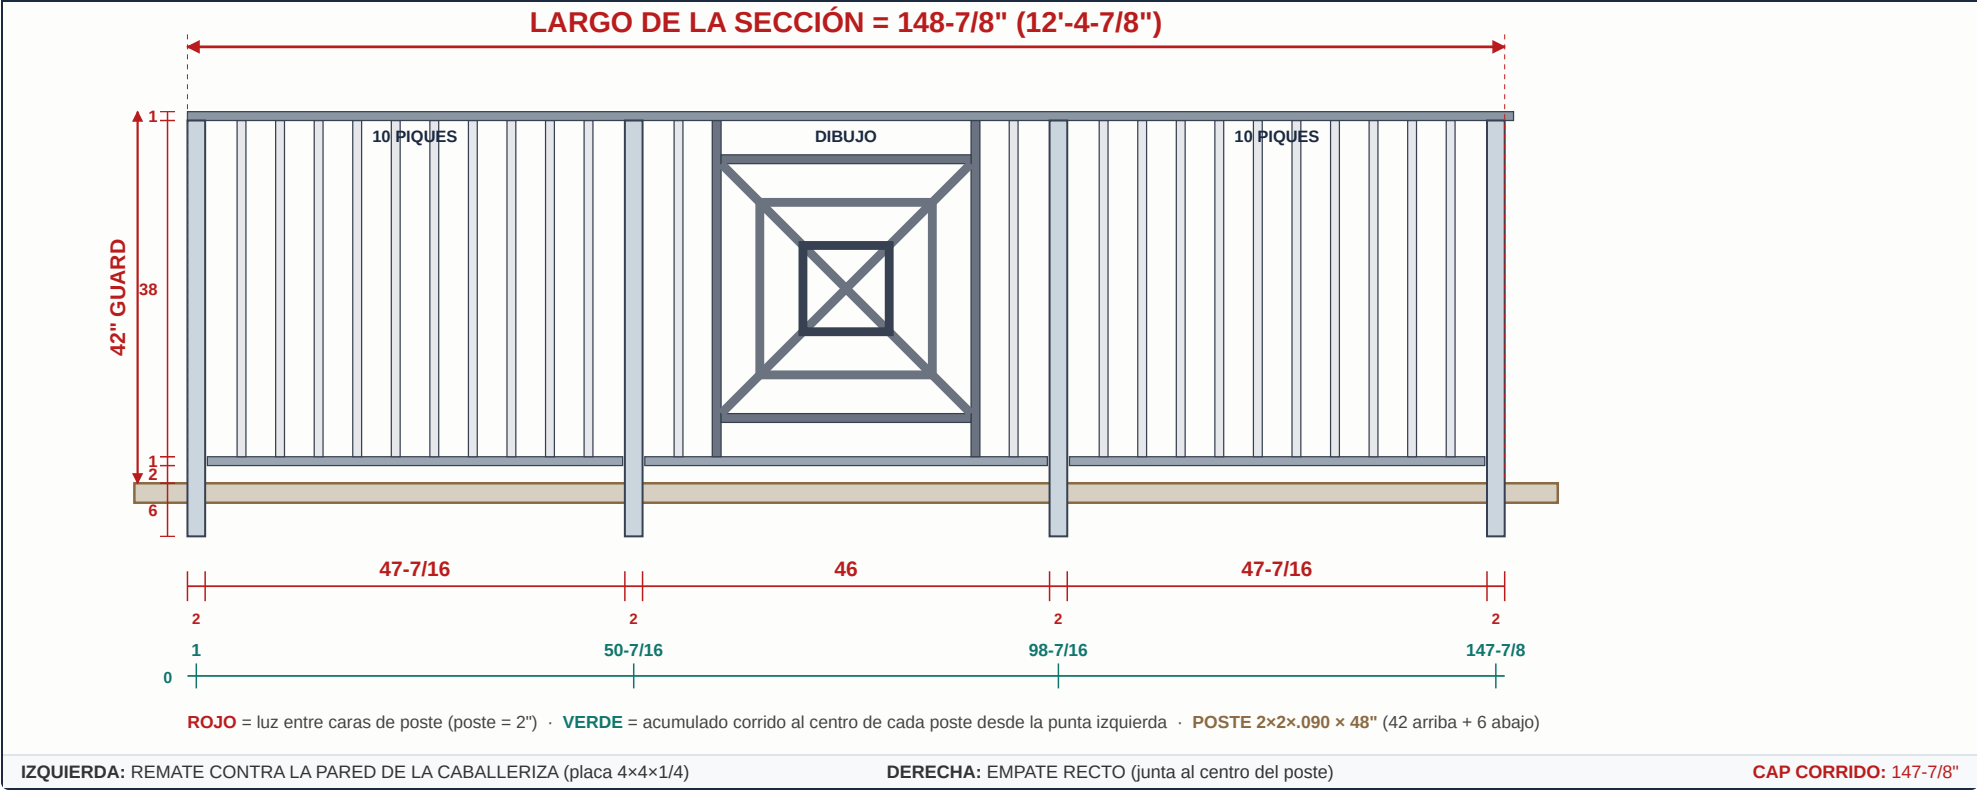

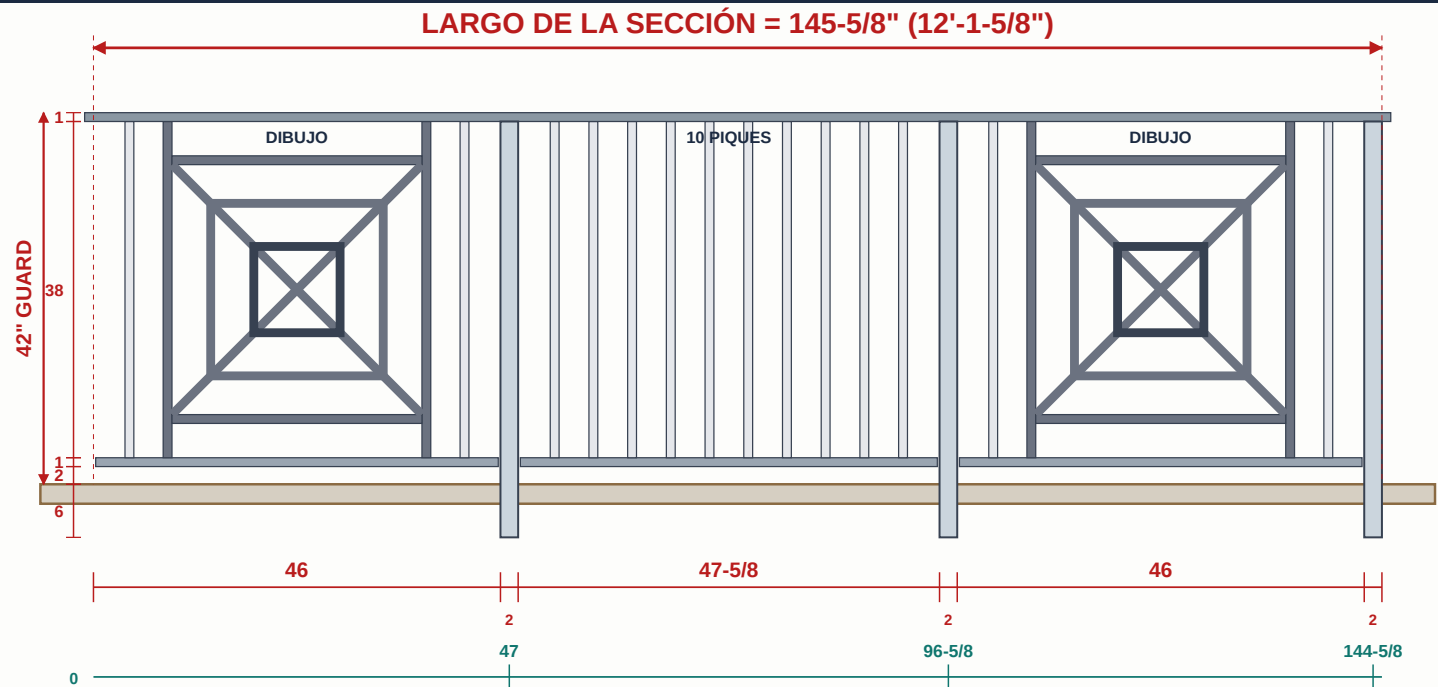


ROJO = luz entre caras de poste (poste = 2") · **VERDE** = acumulado corrido al centro de cada poste desde la punta izquierda · **POSTE 2x2x.090 x 48"** (42 arriba + 6 abajo)

IZQUIERDA: EMPATE RECTO (arranca en paño)

DERECHA: EMPATE RECTO (junta al centro del poste)

CAP CORRIDO: 145-5/8"

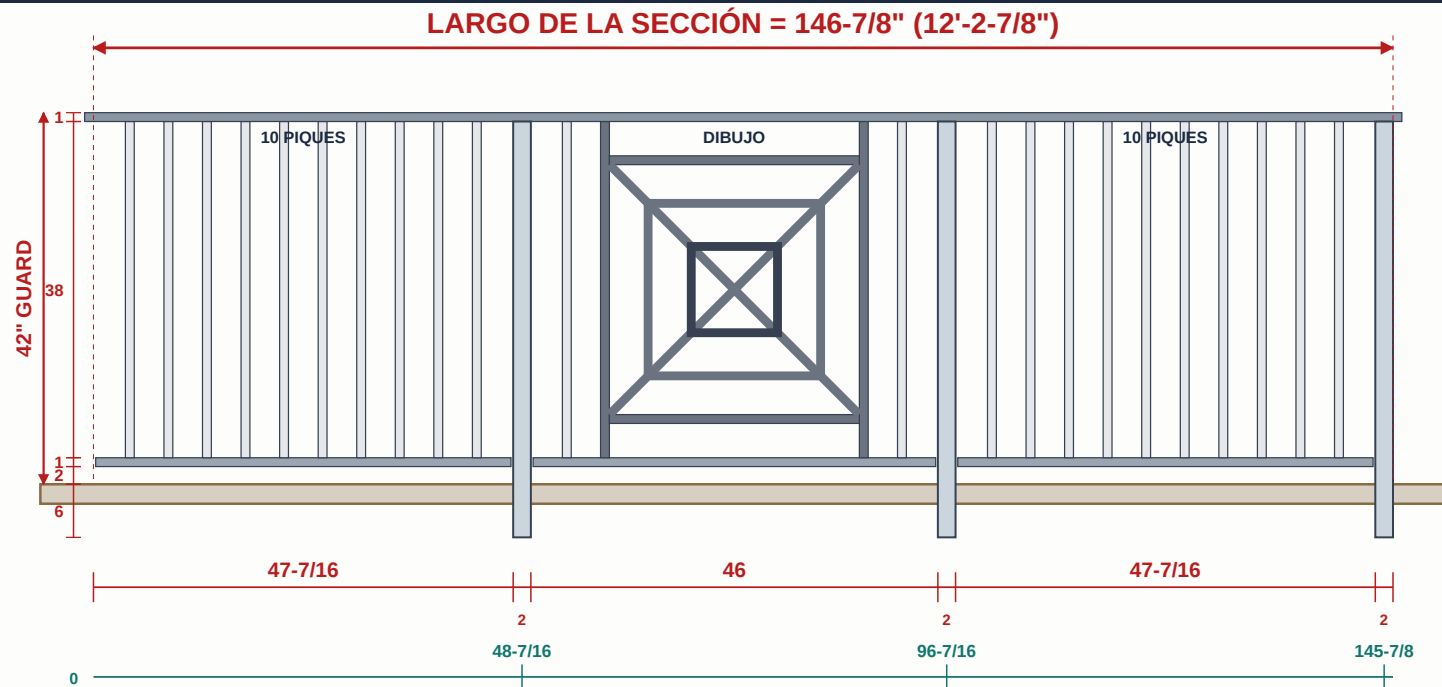


ROJO = luz entre caras de poste (poste = 2") · **VERDE** = acumulado corrido al centro de cada poste desde la punta izquierda · **POSTE** 2×2×.090 × 48" (42 arriba + 6 abajo)

IZQUIERDA: EMPATE RECTO (arranca en paño)

DERECHA: ESQUINA con P-1 (lleva el poste de esquina)

CAP CORRIDO: 147-7/8"

LARGO DE LA SECCIÓN = 189-3/8" (15'-9-3/8")

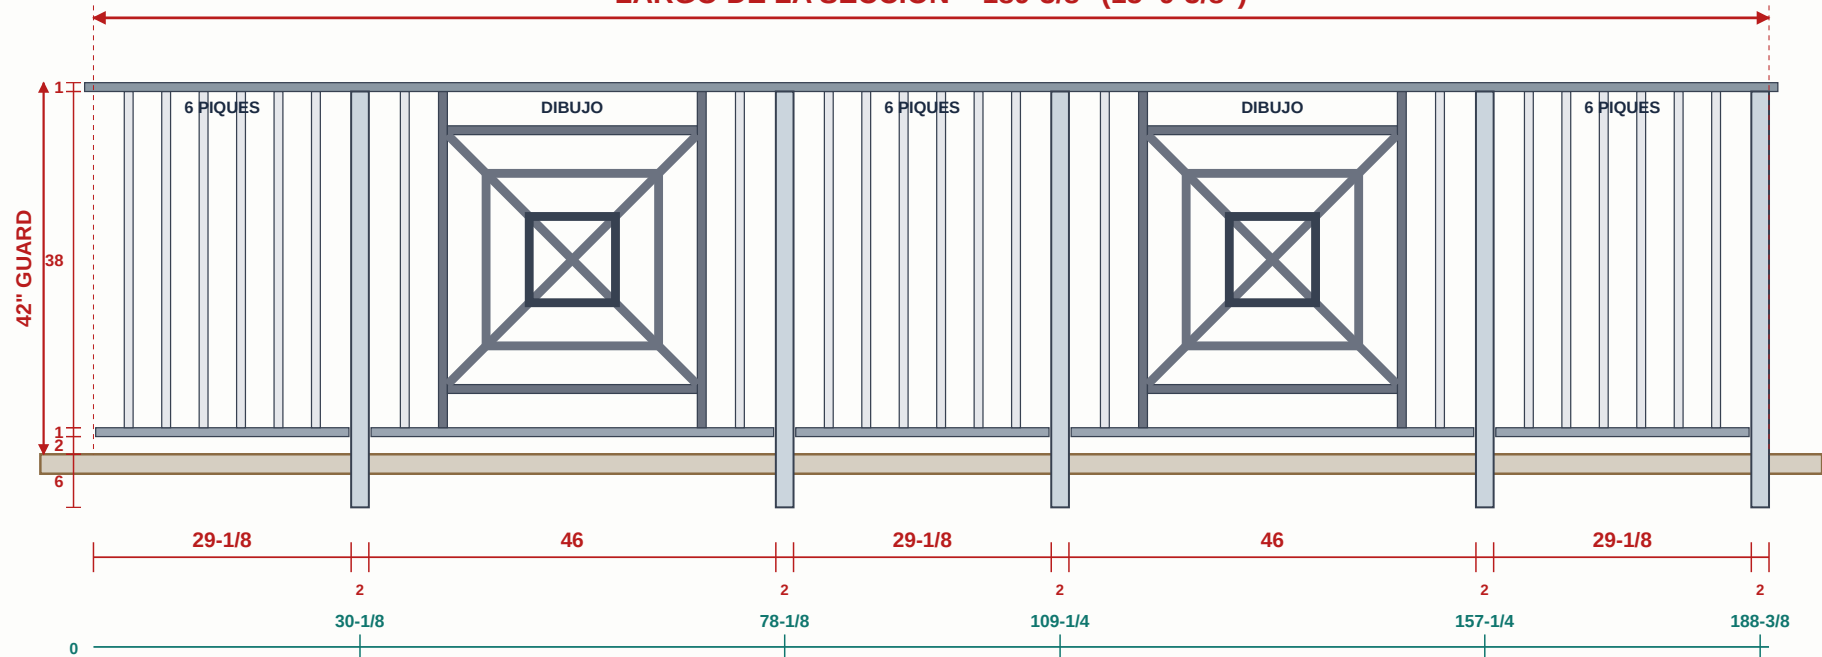


ROJO = luz entre caras de poste (poste = 2") · **VERDE** = acumulado corrido al centro de cada poste desde la punta izquierda · **POSTE** 2×2×.090 × 48" (42 arriba + 6 abajo)

IZQUIERDA: ESQUINA (arranca en paño, apoya en el poste de N-3)

DERECHA: ESQUINA con Q-1 (lleva el poste de esquina)

CAP CORRIDO: 189-3/8"

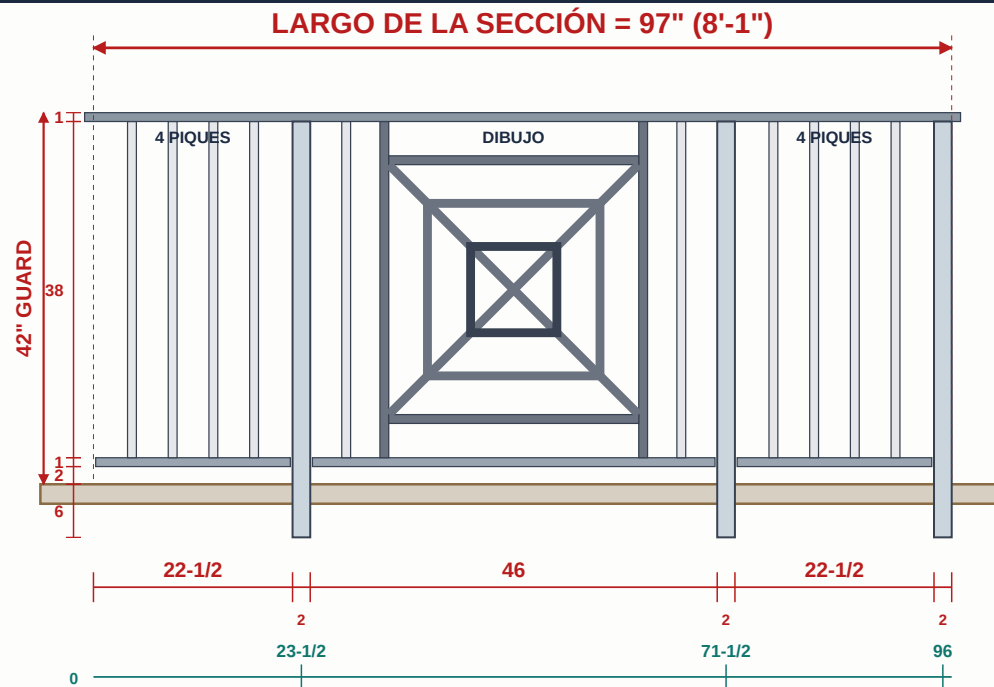


ROJO = luz entre caras de poste (poste = 2") · **VERDE** = acumulado corrido al centro de cada poste desde la punta izquierda · **POSTE 2x2x.090 x 48"** (42 arriba + 6 abajo)

IZQUIERDA: ESQUINA (arranca en paño, apoya en el poste de P-1)

DERECHA: ESQUINA con R-1 (lleva el poste de esquina)

CAP CORRIDO: 97"

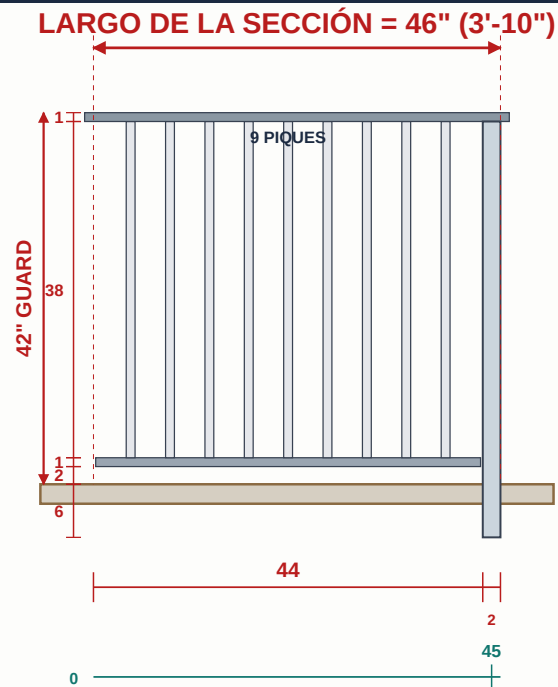

ROJO = luz entre caras de poste (poste = 2") · **VERDE** = acumulado corrido al centro de cada poste desde la punta izquierda · **POSTE 2x2x.090 x 48"** (42 arriba + 6 abajo)

IZQUIERDA: ESQUINA (arranca en paño, apoya en el poste de Q-1)

DERECHA: REMATE CONTRA LA PARED DE LA CABALLERIZA (placa 4x4x1/4)

CAP CORRIDO: 46"

Luz	Panel	Veces	Piques	Luz entre piques	Marcas al CENTRO de cada pique, desde la punta izquierda del riel
47-5/8"	47-1/8"	1	10	~3-3/8"	3-7/8 8-1/4 12-5/8 17 21-3/8 25-3/4 30-1/8 34-1/2 38-7/8 43-1/4
47-7/16"	46-15/16"	4	10	~3-11/32"	3-7/8 8-3/16 12-9/16 16-15/16 21-5/16 25-5/8 30 34-3/8 38-3/4
44"	43-1/2"	1	9	~3-7/16"	3-15/16 8-3/8 12-7/8 17-5/16 21-3/4 26-3/16 30-5/8 35-1/8 39-9/16
29-1/8"	28-5/8"	3	6	~3-7/32"	3-3/4 7-15/16 12-3/16 16-7/16 20-11/16 24-7/8
22-1/2"	22"	2	4	~3-19/32"	4-1/8 8-11/16 13-5/16 17-7/8

Las marcas están redondeadas al **1/16** más cercano y cada una se mide **desde la punta izquierda del riel**, no de pique en pique — así el error no se acumula. La "luz entre piques" es solo de referencia: **manda la marca**.

REGLAS QUE NO SE ROMPEN

- **Todo paño decorado es idéntico: luz 46", panel 45-1/2"**. Todos los dibujitos son intercambiables entre sí y entre los dos edificios.
- **Ninguna esquina ni remate lleva dibujo**. Siempre paño de piques, para poder ajustar en obra.
- **Marcar los piques con el flexómetro corrido** desde la punta izquierda del riel usando la tabla de arriba. No medir de pique en pique: se acumula el error.
- **La sección se suelda completa con sus postes** y los rieles se cortan a la luz exacta.
- **Los empates se hacen en el poste, nunca a media bahía** — ver hoja de detalles D-1 a D-4.
- **Tapar el interior de los tubos antes del horno de power coating** o los insets no entran después.
- **En obra no se suelda nada**. Todo empate es mecánico (tornillos SS316).