

6

SECCIONES

7

PAÑOS DE DIBUJO

10

PAÑOS DE PIQUES

85

PIQUES DE 38"

CÓMO LEER ESTE PLANO

CONEXIÓN

Esa punta se une a otra sección. El poste lo lleva la otra sección — aquí va el riel solo, con su inset. En el dibujo se ve el poste en rayita roja.

ESQUINA

Ahí dobla. El poste sí va en esta sección, completo y soldado.

CONTRA LA PARED

Muere contra la pared. Poste completo, no se toca. La placa se pone en obra.

① ② ③

Número de paño dentro de la sección. Debajo dice si es DIBUJO o cuántos piques lleva.

La única medida del plano es de CENTRO DE POSTE A CENTRO DE POSTE. Todo paño de dibujo es 48" centro a centro, siempre, en los dos edificios.

CORTE RECTO DE 38" DE ESTA HOJA

85 piques de los paños + 28 de los dibujos (las 2 V y las 2 B de cada uno) = 113 piezas de 38" rectas. Todas salen del mismo corte, se pican de corrido.


MARCAS DE LOS PIQUES — MEDIR DESDE LA PUNTA IZQUIERDA DEL RIEL

Paño C–C	Riel	Piques	Marca al centro de cada pique
49-5/8"	47-1/8"	10	3-7/8 8-1/4 12-5/8 17 21-3/8 25-3/4 30-1/8 34-1/2 38-7/8 43-1/4
49-7/16"	46-15/16"	10	3-7/8 8-3/16 12-9/16 16-15/16 21-5/16 25-5/8 30 34-3/8 38-3/4 43-1/16
46-11/16"	44-3/16"	9	4 8-9/16 13-1/16 17-9/16 22-1/8 26-5/8 31-1/8 35-5/8 40-3/16
46"	43-1/2"	9	3-15/16 8-3/8 12-7/8 17-5/16 21-3/4 26-3/16 30-5/8 35-1/8 39-9/16
24-1/2"	22"	4	4-1/8 8-11/16 13-5/16 17-7/8

Cada marca se mide desde la misma punta del riel, no de pique en pique. Así no se corre el error.

N-1 CABALLERIZA LADO 2

1 dibujo + 2 de piques

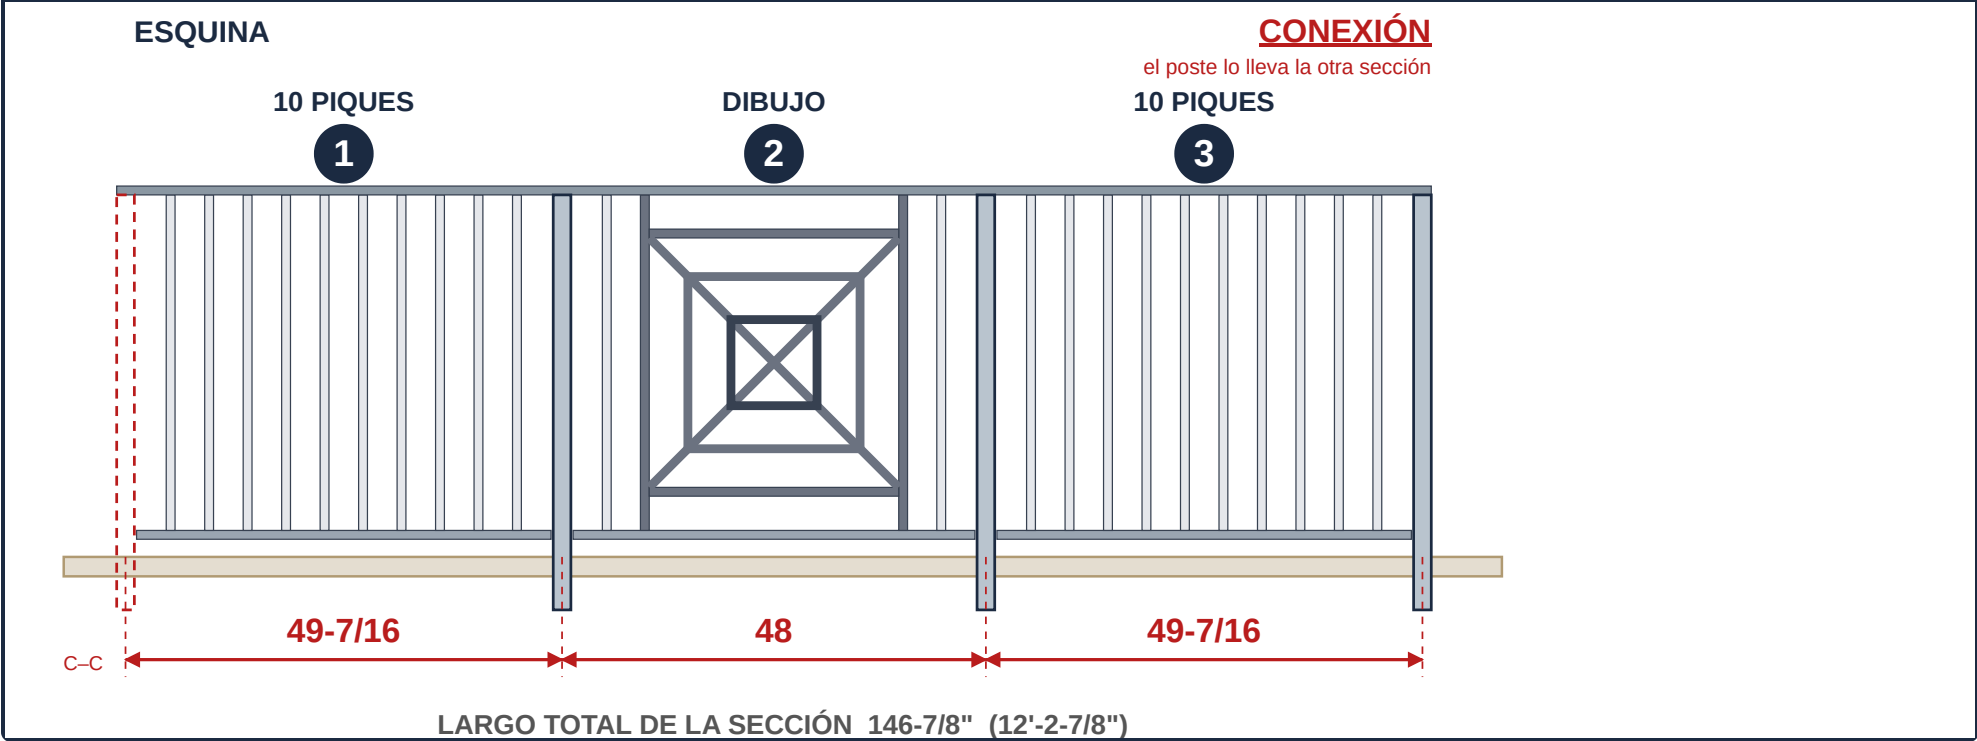

CONEXIÓN

el poste lo lleva la otra sección

DIBUJO

1

10 PIQUES


2

CONEXIÓN

el poste lo lleva la otra sección

DIBUJO

3

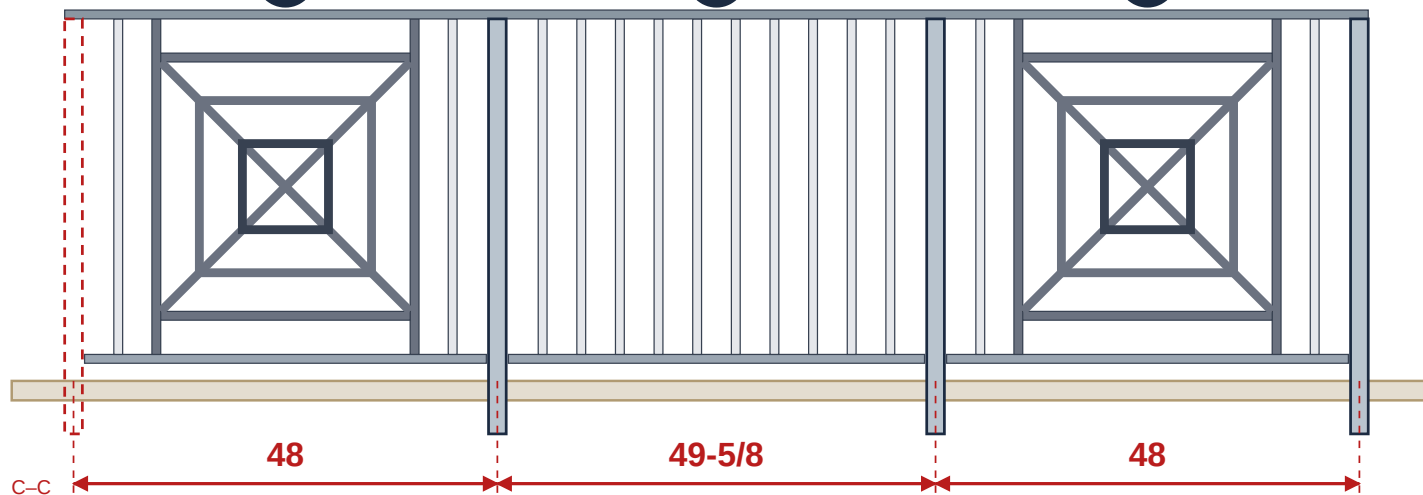

LARGO TOTAL DE LA SECCIÓN 145-5/8" (12'-1-5/8")

CONEXIÓN

el poste lo lleva la otra sección

ESQUINA

10 PIQUES


1

DIBUJO

2

10 PIQUES

3

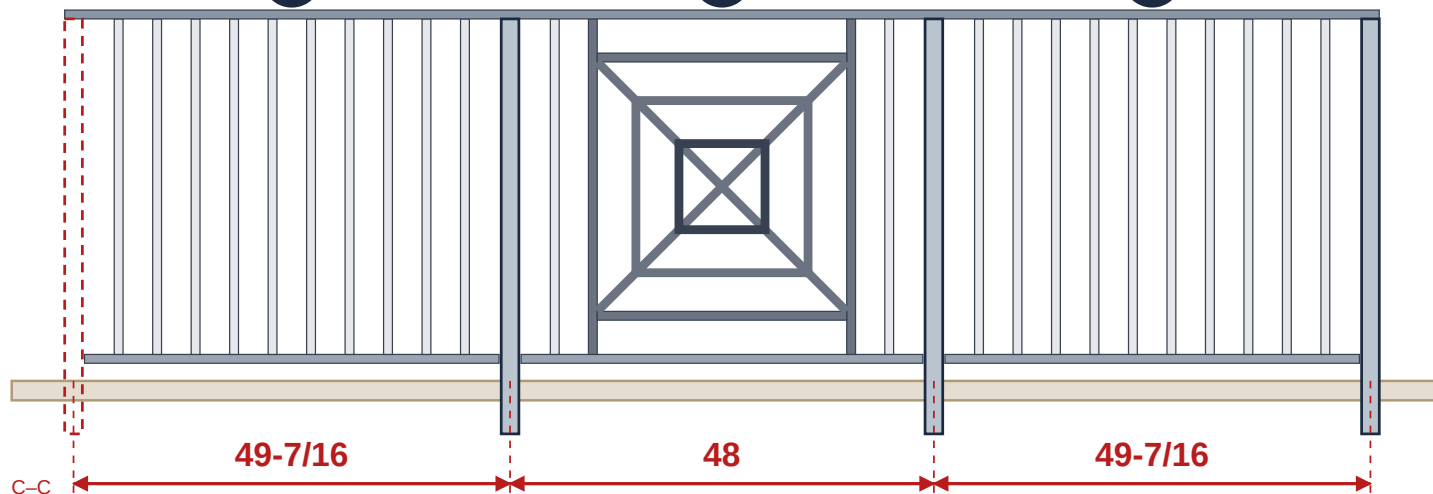

LARGO TOTAL DE LA SECCIÓN 146-7/8" (12'-2-7/8")

CONTRA LA PARED

poste completo, no se toca

ESQUINA

DIBUJO

1

9 PIQUES


2

DIBUJO


3

9 PIQUES

4

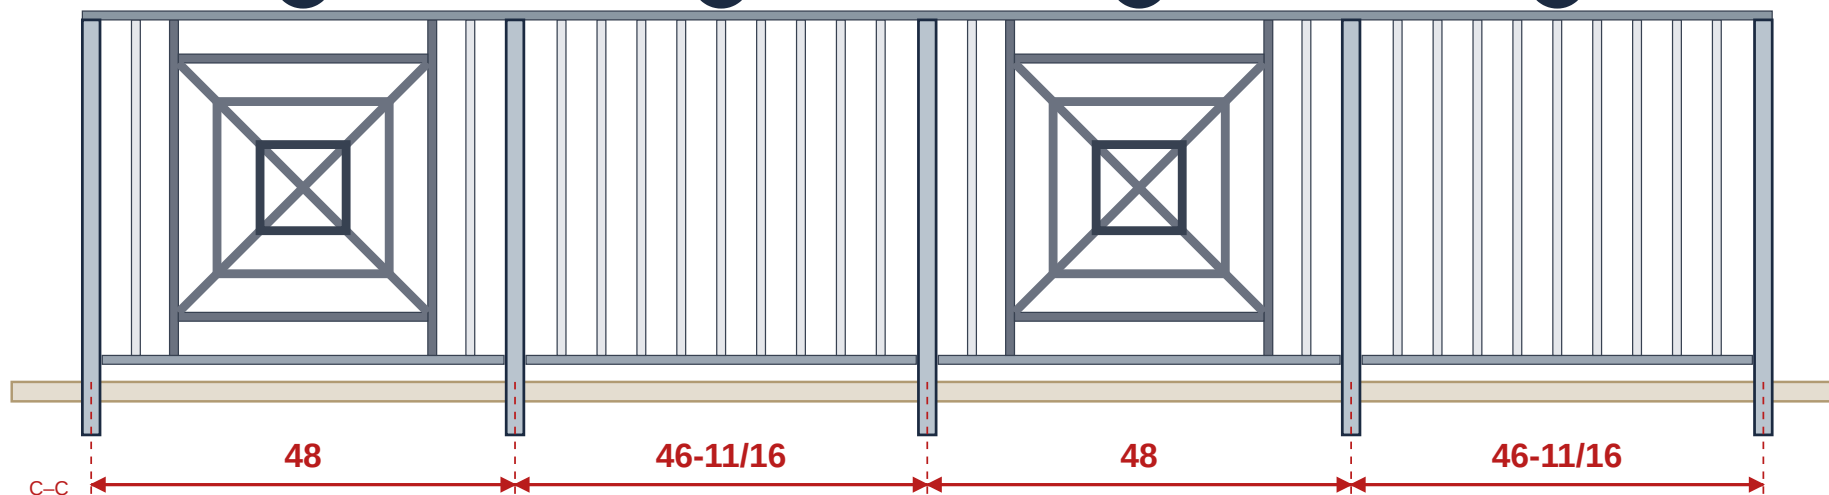

LARGO TOTAL DE LA SECCIÓN 191-3/8" (15'-11-3/8")

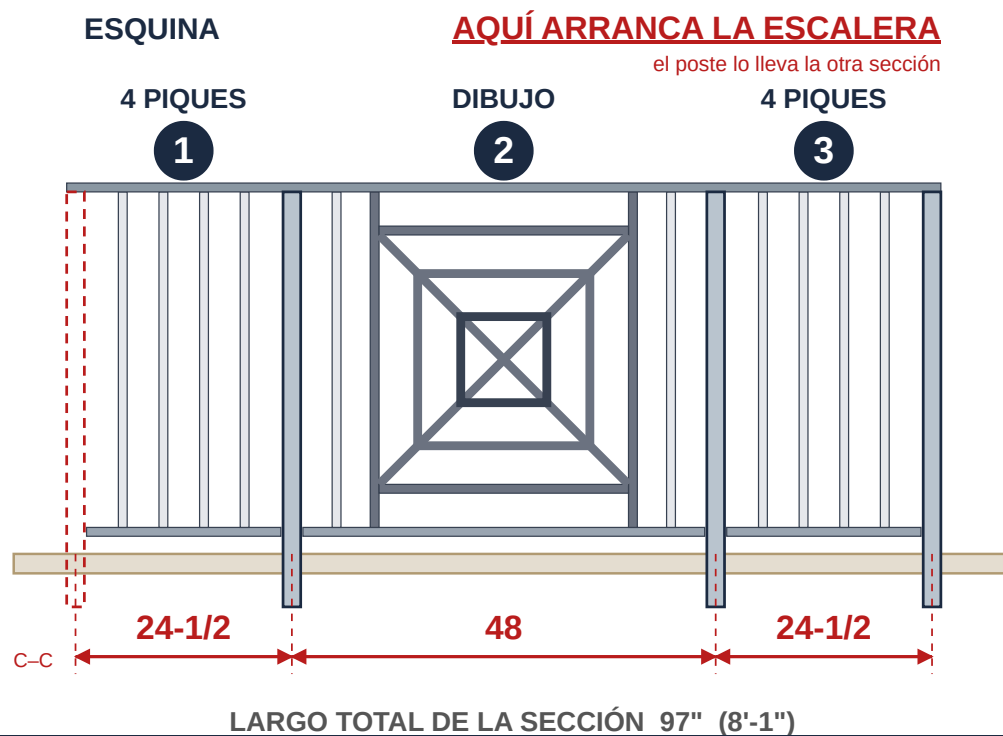


AQUÍ ARRANCA LA ESCALERA CONTRA LA PARED

el poste lo lleva la otra sección

poste completo, no se toca

9 PIQUES

1

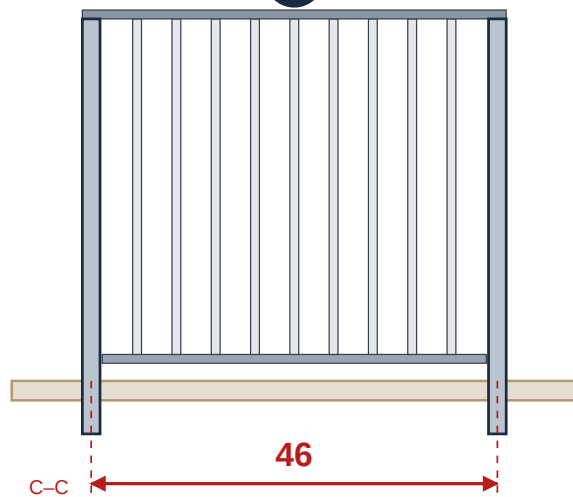

LARGO TOTAL DE LA SECCIÓN 48" (4'-0")