

6

SECCIONES

7

PAÑOS DE DIBUJO

10

PAÑOS DE PIQUES

85

PIQUES DE 38"

CÓMO LEER ESTE PLANO

CONEXIÓN

Esa punta se une a otra sección. El poste lo lleva la otra sección — aquí va el riel solo, con su inset. En el dibujo se ve el poste en rayita roja.

ESQUINA

Ahí dobla. El poste sí va en esta sección, completo y soldado.

CONTRA LA PARED

Muere contra la pared. Poste completo, no se toca. La placa se pone en obra.

① ② ③

Número de paño dentro de la sección. Debajo dice si es DIBUJO o cuántos piques lleva.

La única medida del plano es de CENTRO DE POSTE A CENTRO DE POSTE. Casi todo paño de dibujo es 48" centro a centro. Uno solo es distinto: el de la corrida L de la caballeriza 1 va a 45" centro a centro (bahía de 43"), con el riel de 42-1/2" en vez de 45-1/2. Manda la cota del dibujo, no esta nota.

CORTE RECTO DE 38" DE ESTA HOJA

85 piques de los paños + 28 de los dibujos (las 2 V y las 2 B de cada uno) = 113 piezas de 38" rectas. Todas salen del mismo corte, se pican de corrido.

MARCAS DE LOS PIQUES — MEDIR DESDE LA PUNTA IZQUIERDA DEL RIEL

Paño C–C	Riel	Piques	Marca al centro de cada pique									
49-5/8"	47-5/8"	10	3-15/16	8-5/16	12-3/4	17-3/16	21-5/8	26	30-7/16	34-7/8		
			39-5/16	43-11/16								
49-7/16"	47-7/16"	10	3-7/8	8-5/16	12-11/16	17-1/8	21-1/2	25-15/16	30-5/16	34-		
			3/4	39-1/8	43-9/16							
46-11/16"	44-11/16"	9	4-1/16	8-5/8	13-3/16	17-3/4	22-3/8	26-15/16	31-1/2	36-1/16		
				40-5/8								
46"	44"	9	4	8-1/2	13	17-1/2	22	26-1/2	31	35-1/2	40	
24-1/2"	22-1/2"	4	4-3/16	8-7/8	13-5/8	18-5/16						

Cada marca se mide desde la misma punta del riel, no de pique en pique. Así no se corre el error.

N-1 CABALLERIZA LADO 2

1 dibujo + 2 de piques

ESQUINA → P-1


CONEXIÓN

el poste lo lleva la otra sección

10 PIQUES

DIBUJO

10 PIQUES

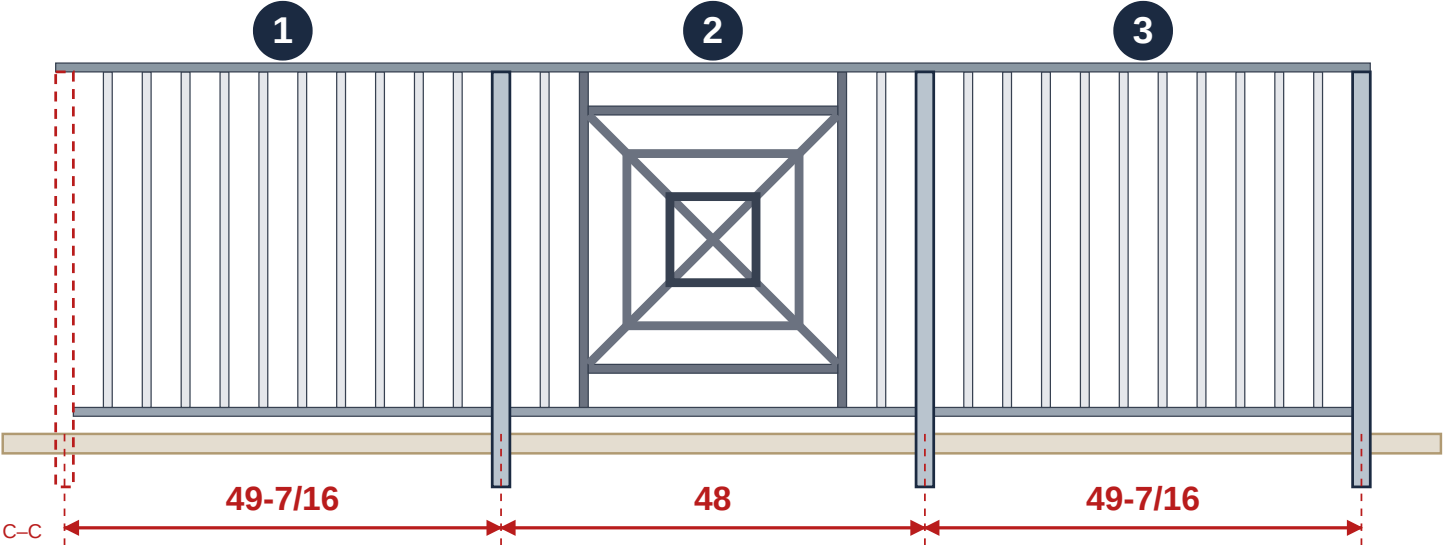

LARGO TOTAL DE LA SECCIÓN 146-7/8" (12'-2-7/8")

CONEXIÓN

el poste lo lleva la otra sección

DIBUJO

1

10 PIQUES


2

CONEXIÓN

el poste lo lleva la otra sección

DIBUJO

3

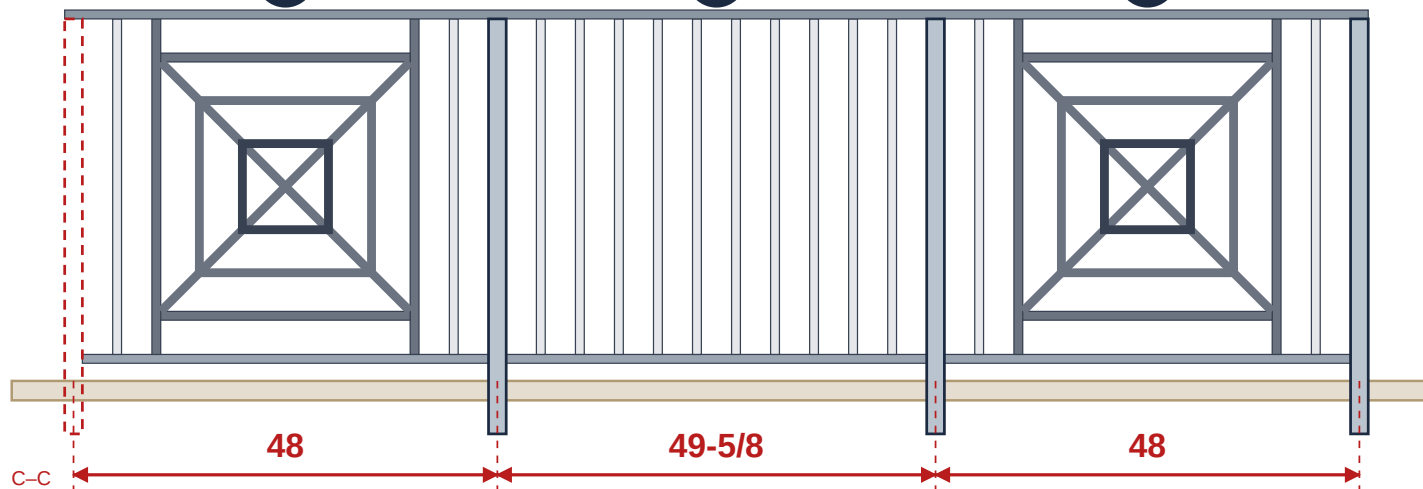

LARGO TOTAL DE LA SECCIÓN 145-5/8" (12'-1-5/8")

CONEXIÓN

el poste lo lleva la otra sección

ESQUINA

10 PIQUES


1

DIBUJO

2

10 PIQUES

3

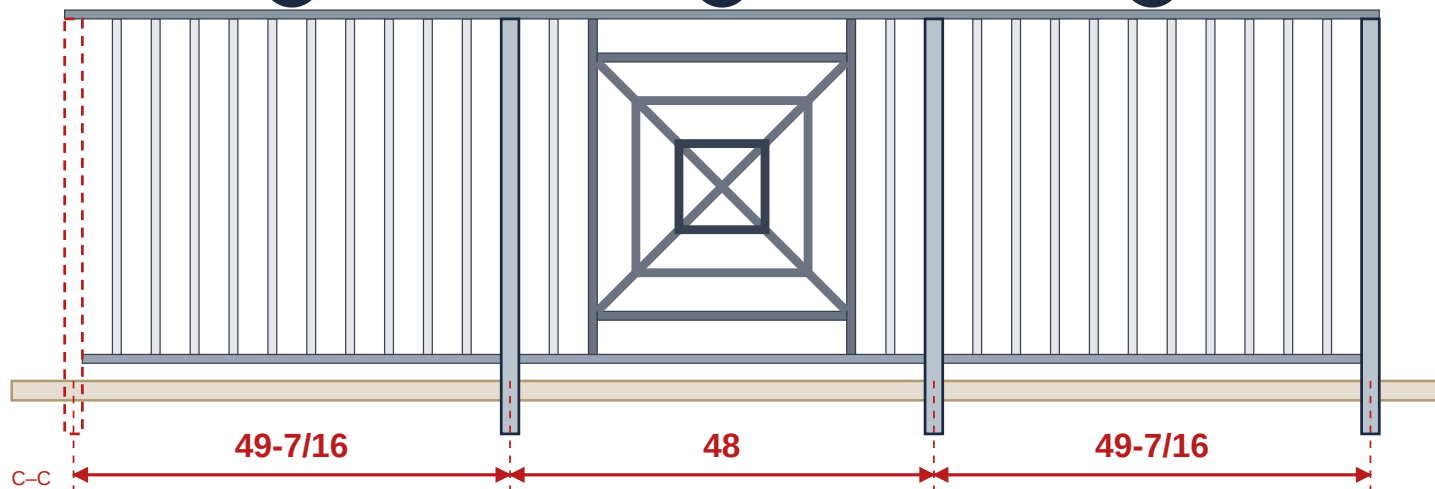

LARGO TOTAL DE LA SECCIÓN $146\frac{7}{8}$ " (12'-2-7/8")

CONTRA LA PARED

poste completo, no se toca

ESQUINA → N-1

DIBUJO

1

9 PIQUES


2

DIBUJO

3

9 PIQUES


4

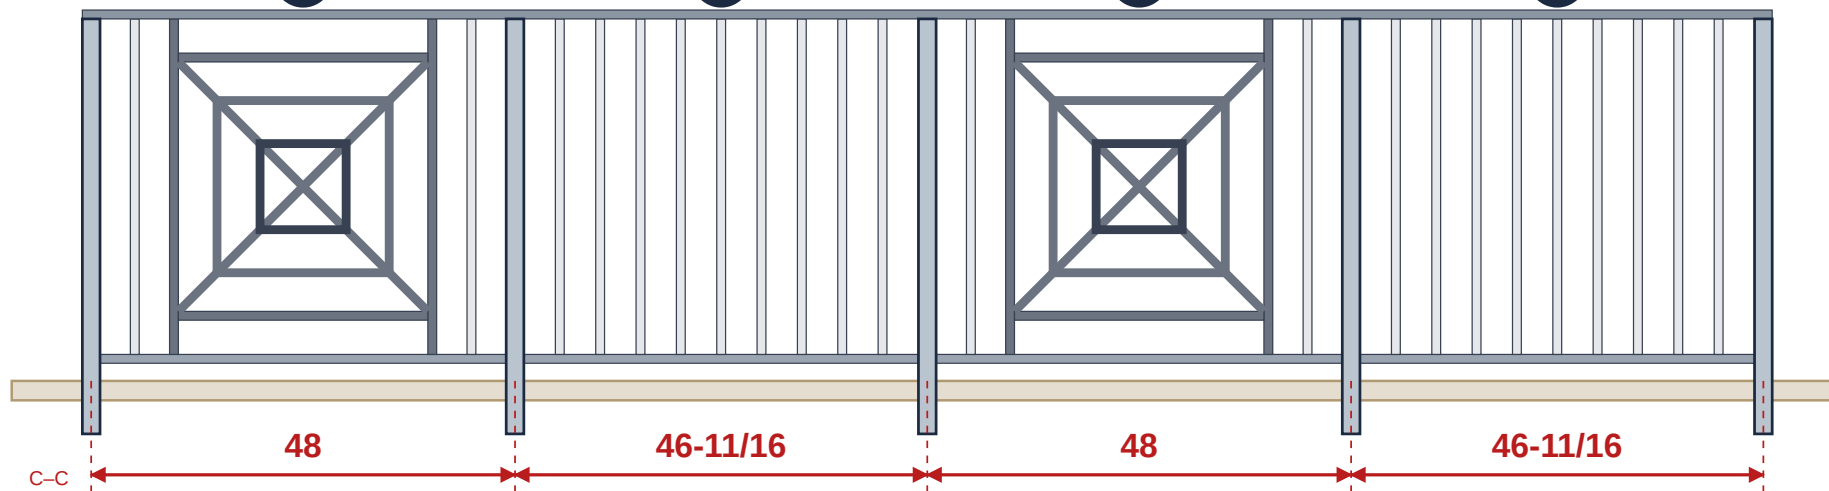

LARGO TOTAL DE LA SECCIÓN 191-3/8" (15'-11-3/8")

AQUÍ ARRANCA LA ESCALERA

el poste lo lleva la otra sección

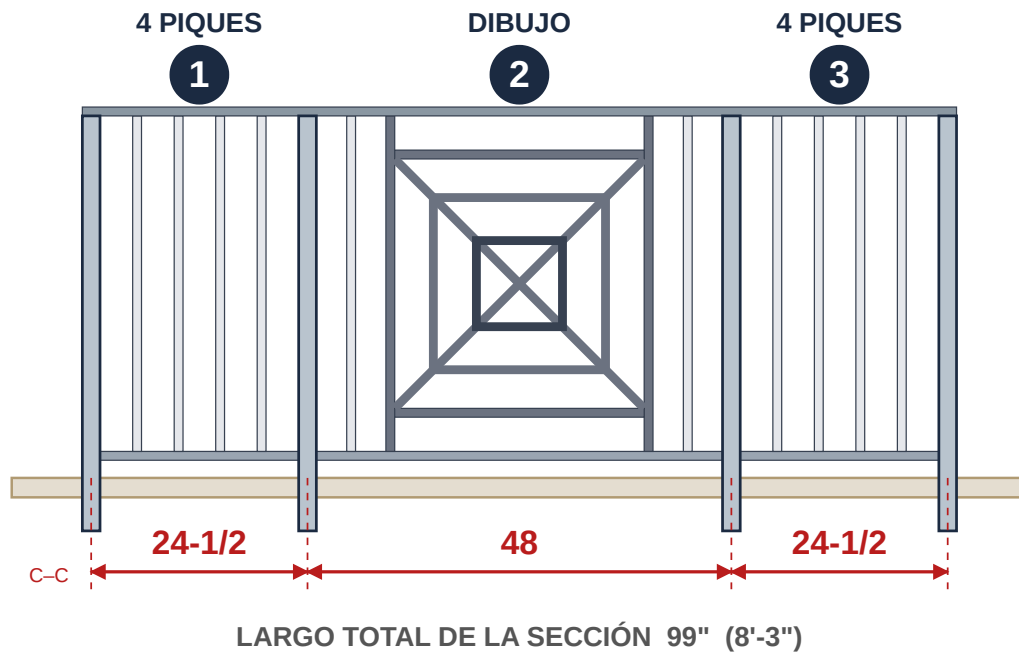


AQUÍ ARRANCA LA ESCALERA CONTRA LA PARED

el poste lo lleva la otra sección

poste completo, no se toca

9 PIQUES

1

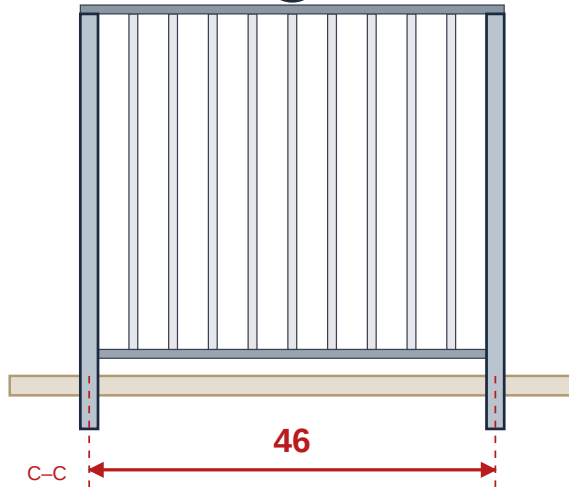

LARGO TOTAL DE LA SECCIÓN 48" (4'-0")